


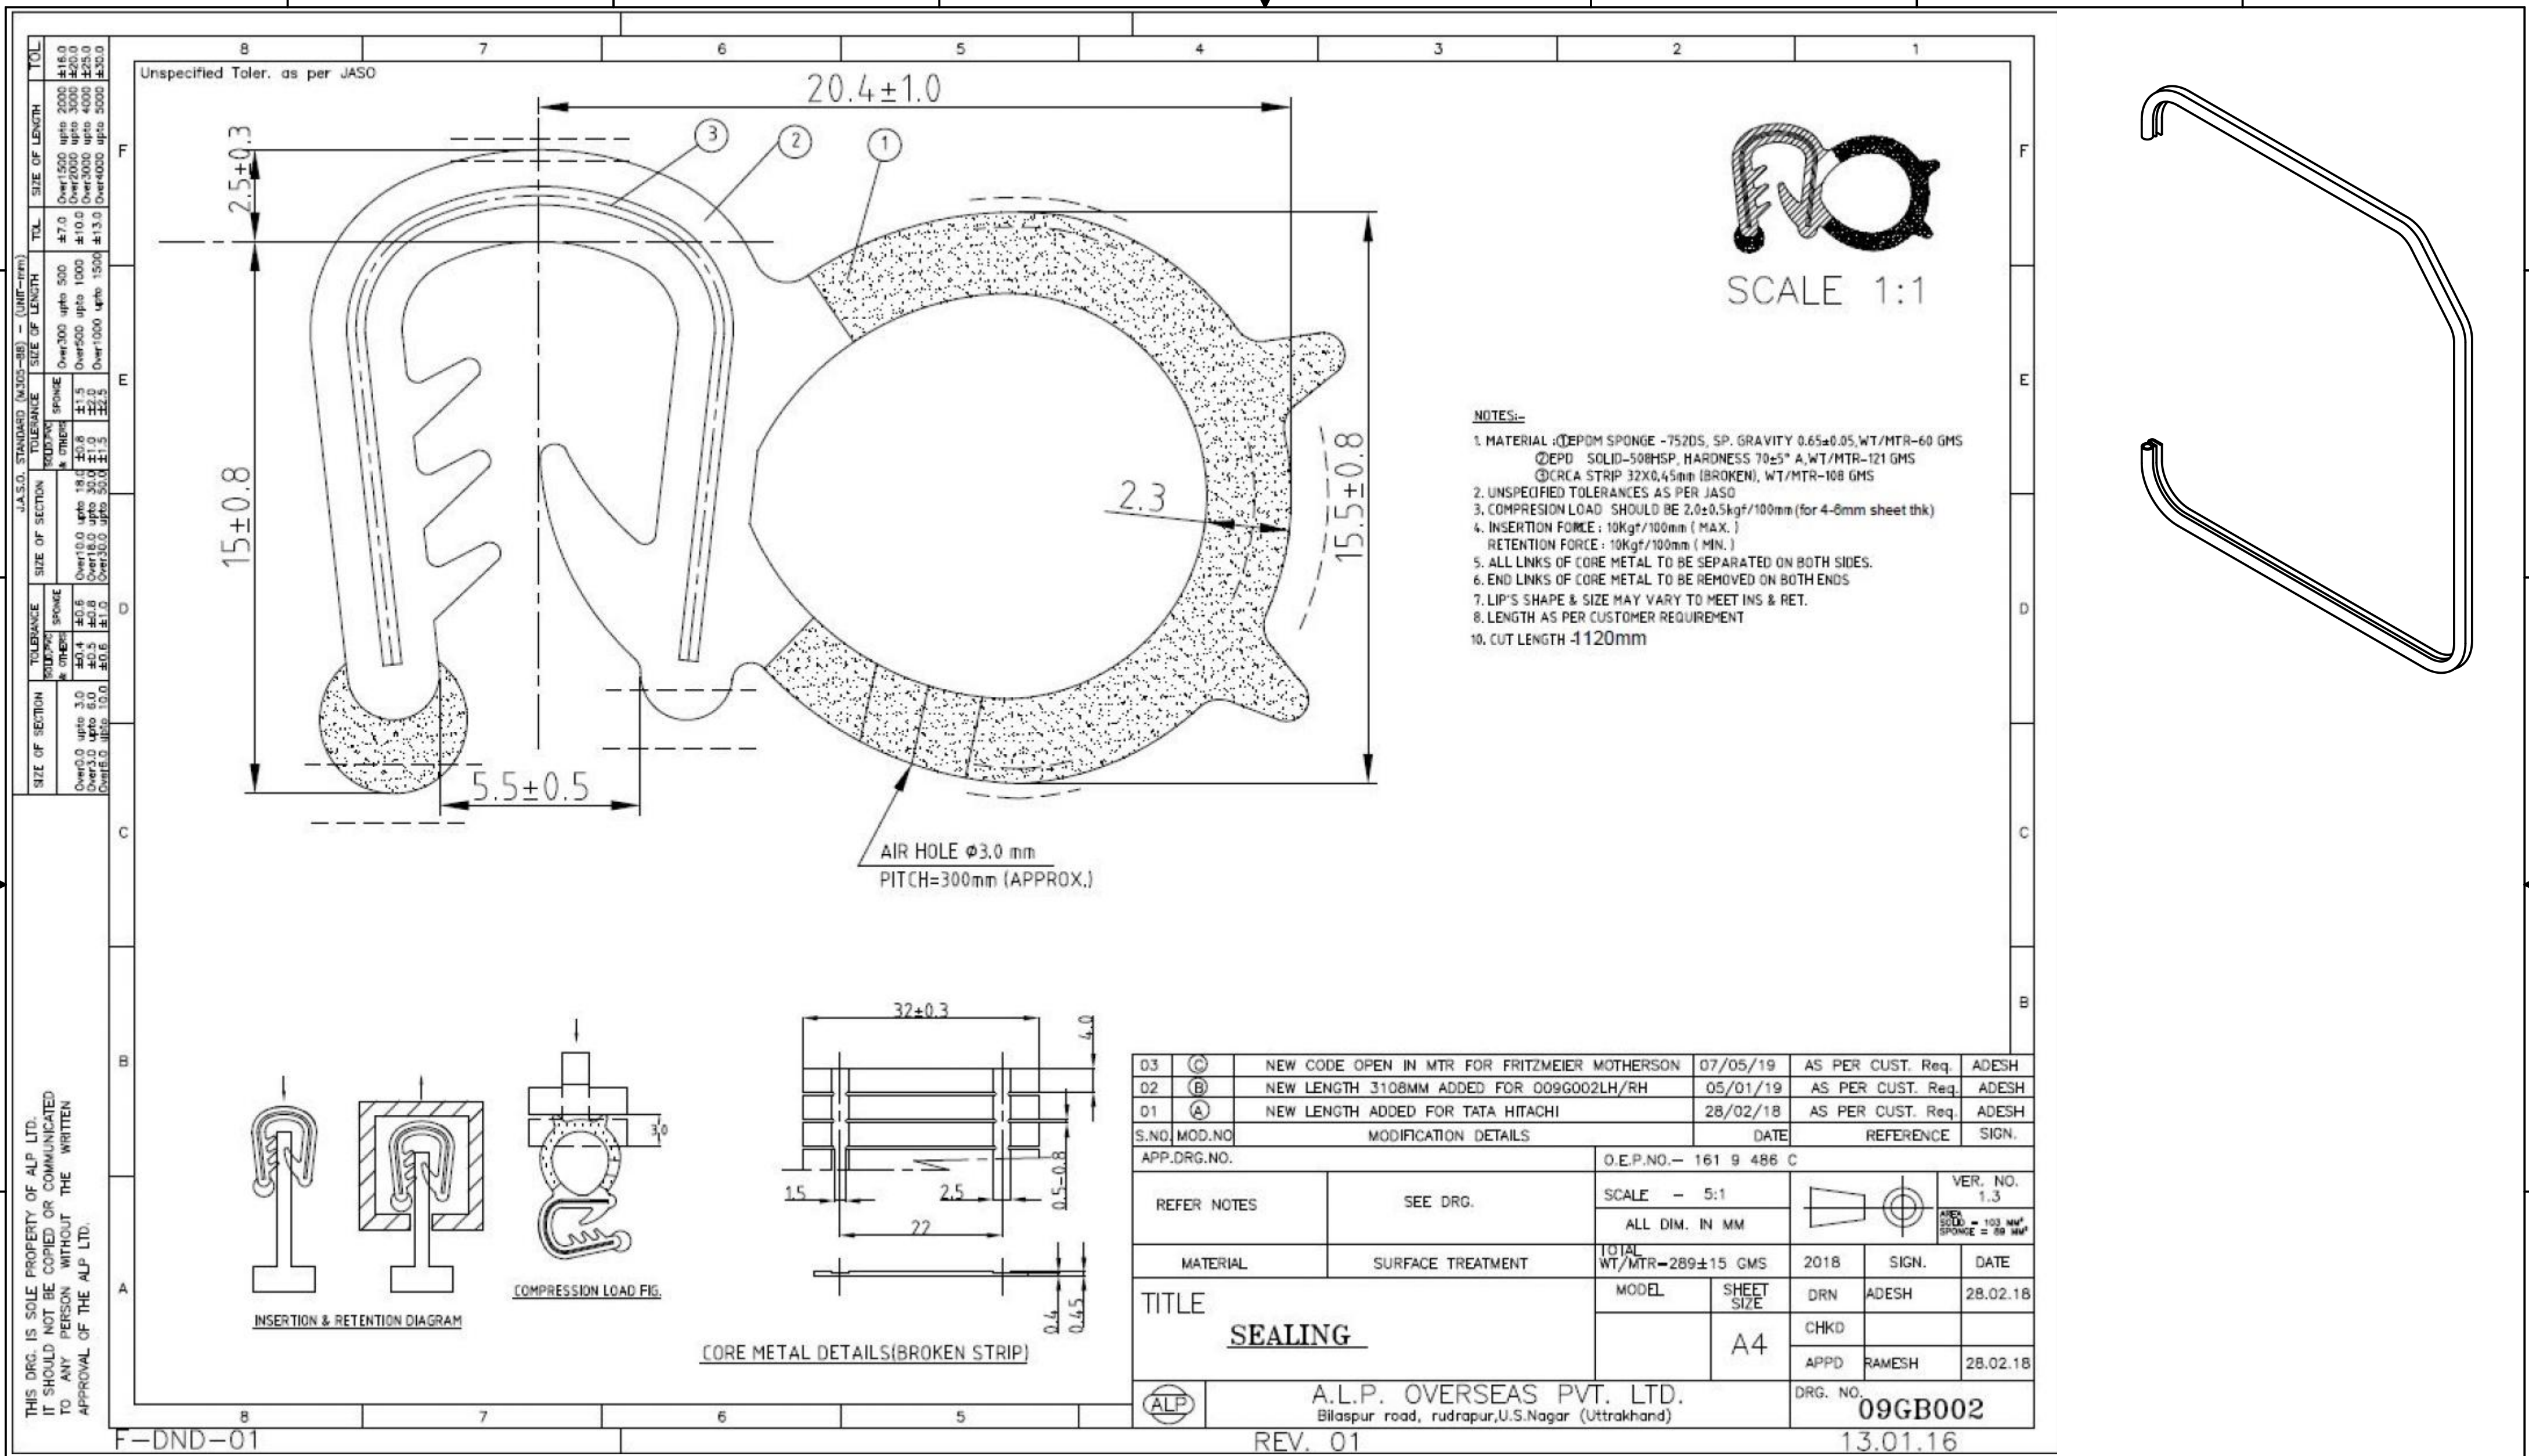

NOTES: 1. ENGINEERING APPROVED SOURCE: SUPPLIER NAME: ALP OVERSEAS PVT. LTD. SUPPLIER PART NUMBER: 09GB002 2. SUPPLIER APPROVAL ON FILE FOR UNRESTRICTED CIRCULATION PER DWGA125. 3. BEADING LENGTH: 2000 mm	
--	--	